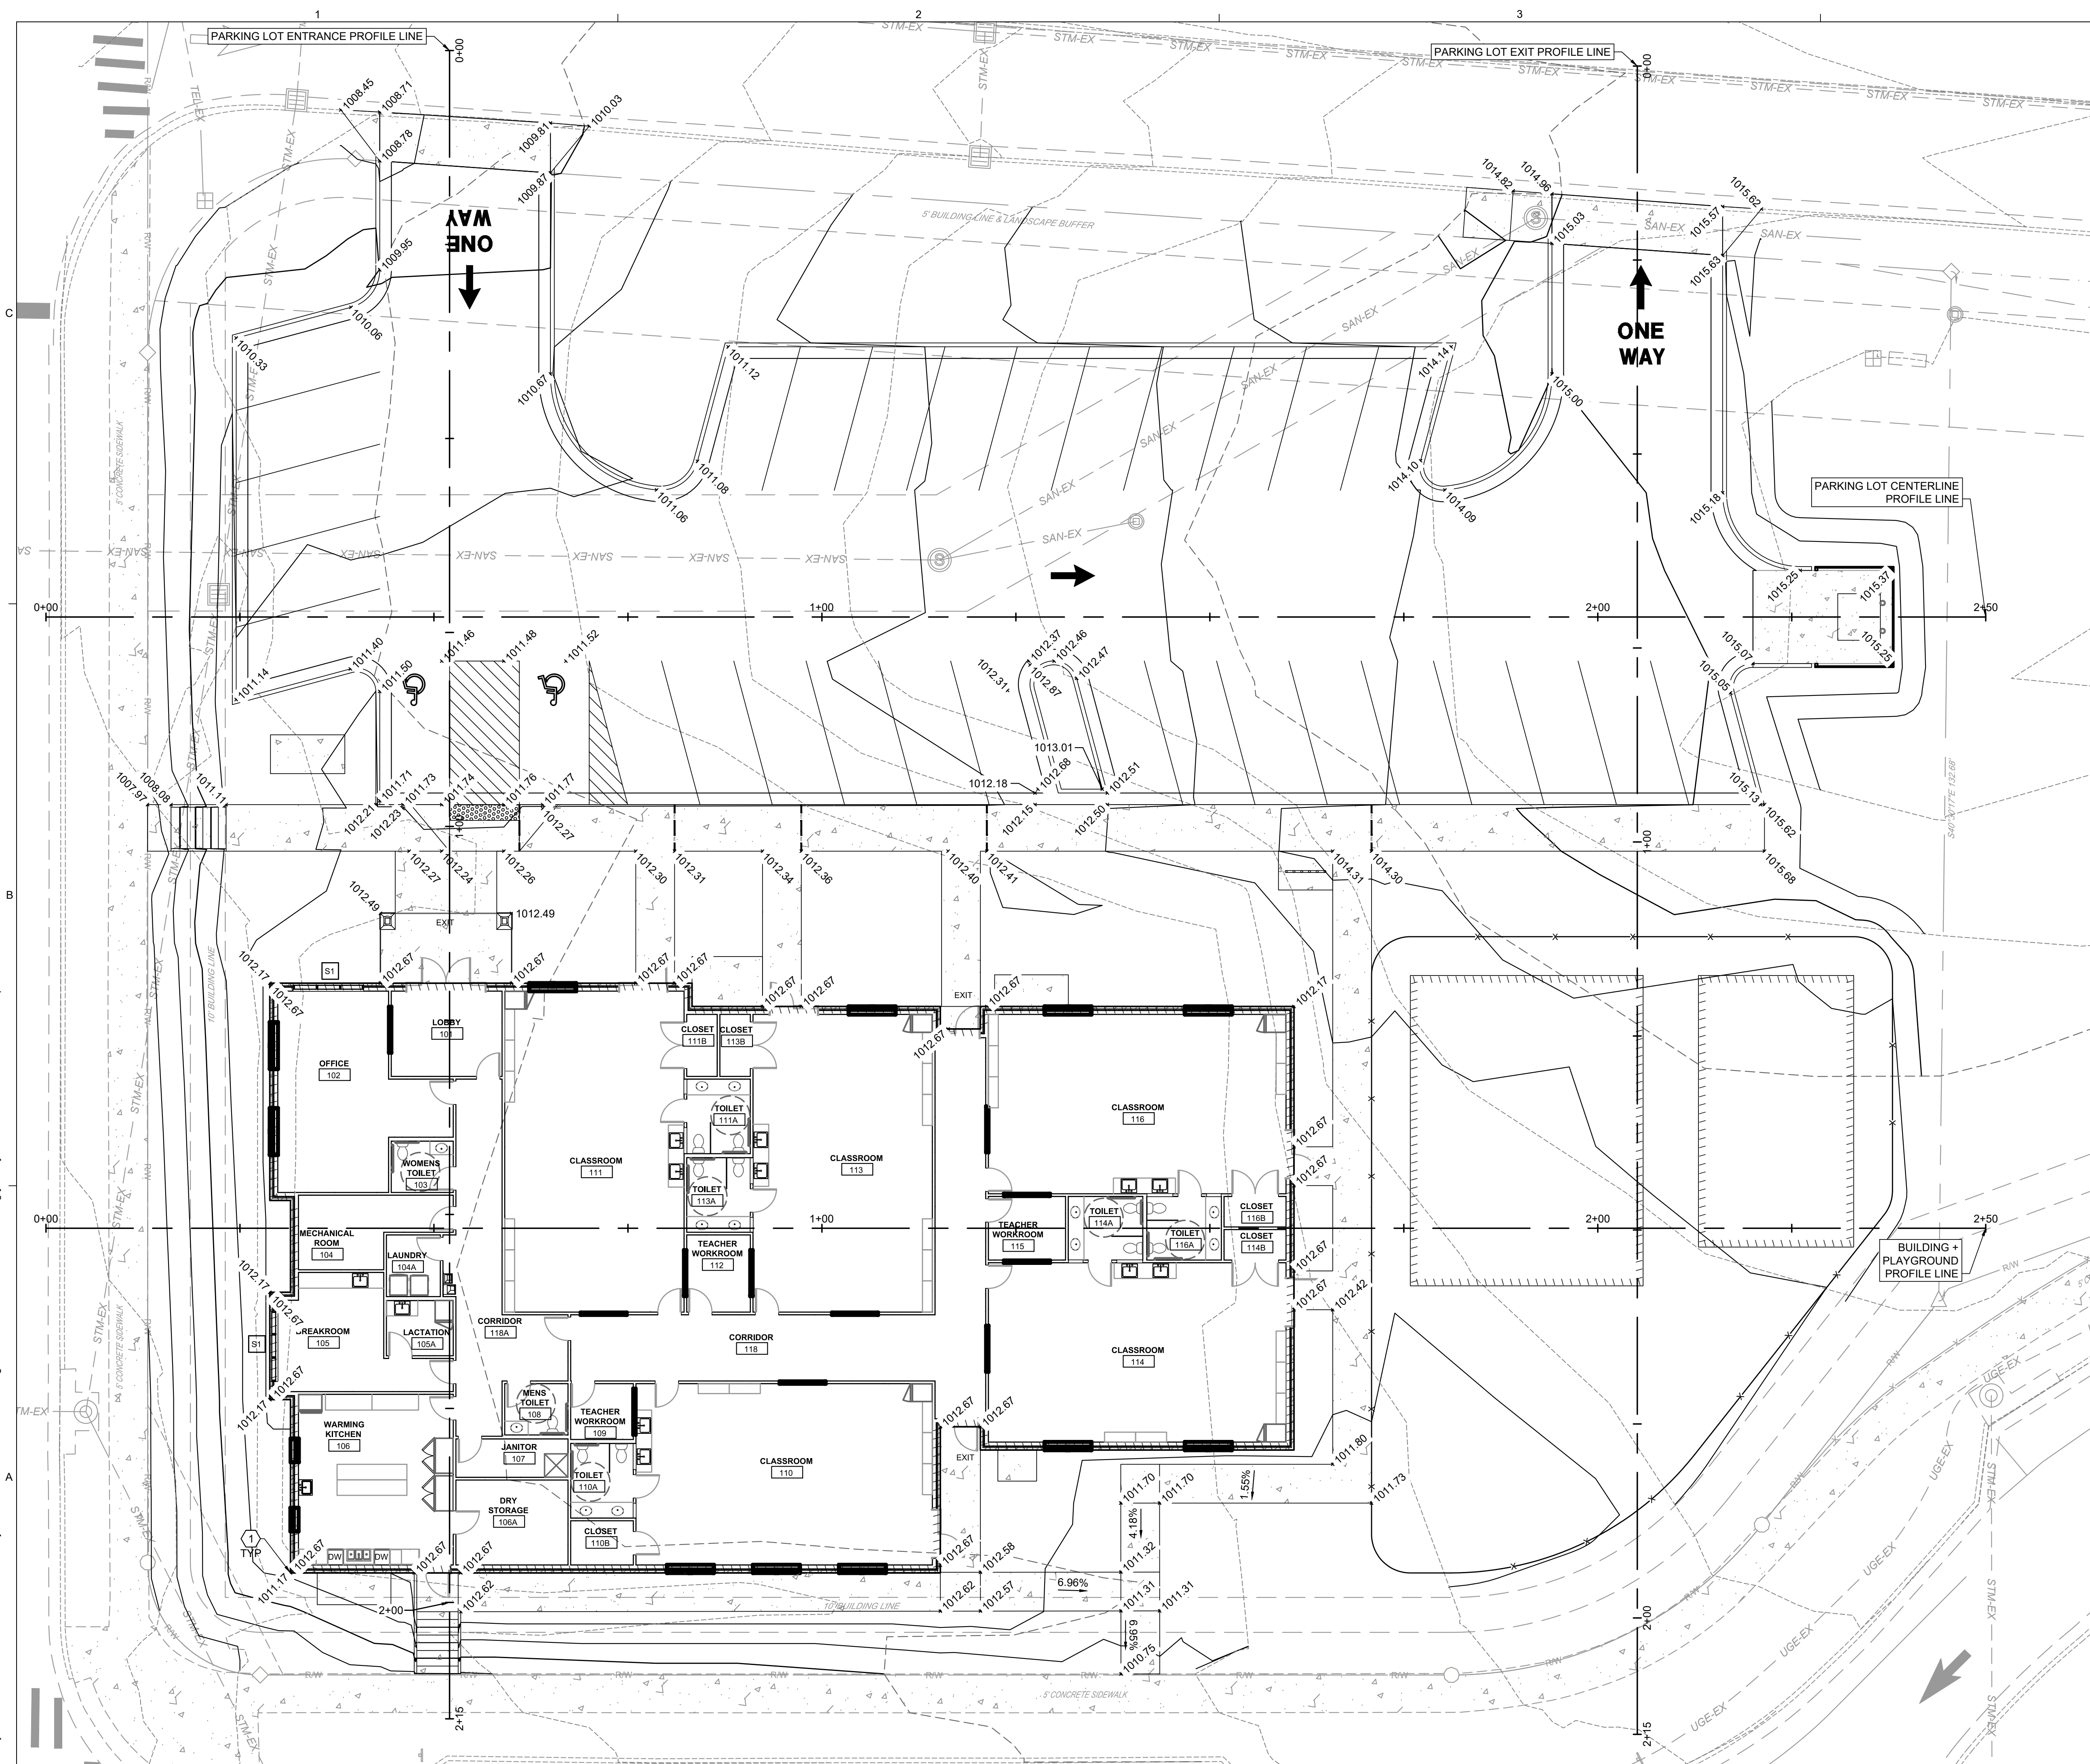




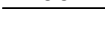
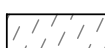
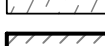
GENERAL NOTES

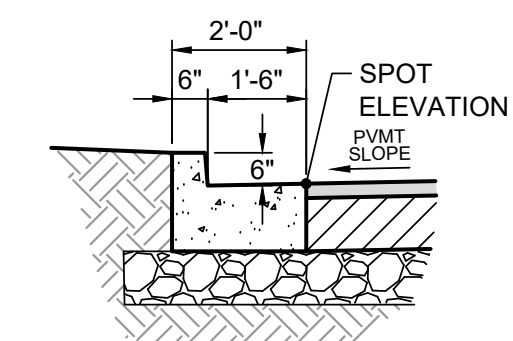
- A. STRAIGHT GRADE BETWEEN SPOT ELEVATIONS IN ALL PAVED AREAS.
- B. SPOT ELEVATIONS ARE SHOWN AT THE BOTTOM OF CURB UNLESS OTHERWISE NOTED. SPOT ELEVATIONS NOTED AS "TC" ARE AT TOP OF SIDEWALK/CONCRETE. SPOT ELEVATIONS NOTED AS "TW" ARE AT THE TOP OF RETAINING WALL.
- C. FOR CLARITY, UNDERGROUND UTILITIES ARE NOT SHOWN ON THIS PLAN. REFER TO SITE DRAINAGE DRAWINGS FOR DETAILS.

GRADING KEYNOTES

1. 1.5' FOUNDATION WALL

MAP LEGEND

- | | |
|--|--|
|  | BUILDING LINE |
|  | PROPERTY LINE |
|  | EXISTING CONTOUR |
|  | PROPOSED CONTOUR |
| (TC) | TOP OF CURB ELEVATION |
| (ME) | MATCH EXISTING ELEVATION |
|  | DRAINAGE FLOW ARROW |
|  | SLOPE GRADE |
|  | PROVIDE CONCRETE SIDEWALK |
|  | PROVIDE HEAVY-DUTY CONCRETE |
|  | PROPOSED BUILDING |
|  | CURB CUT WITH TAPER 12" WIDE
INSTALL RIP RAP PER PLAN |



CURB & GUTTER
SPOT ELEV REFERENCE

NTS
UNLESS OTHERWISE NOTED, ALL SPOT
ELEVATIONS ARE TO FINISHED GRADE.

DATE : 02/11/2026
PROJECT NO. : 240895
DESIGNED BY : PDC
DRAWN BY : PDC
SCALE : AS NOTED

[illegible]

THIS DRAWING NOT RELEASED FOR
CONSTRUCTION UNLESS SO NOTED ABOVE

SHEET TITLE

GRADING PLAN



C-201

LIC. No.
DATE:

—
SHEET